



M=40310
P=164150

M=40260
P=164150

M=40310
P=164090

M=40260
P=164090

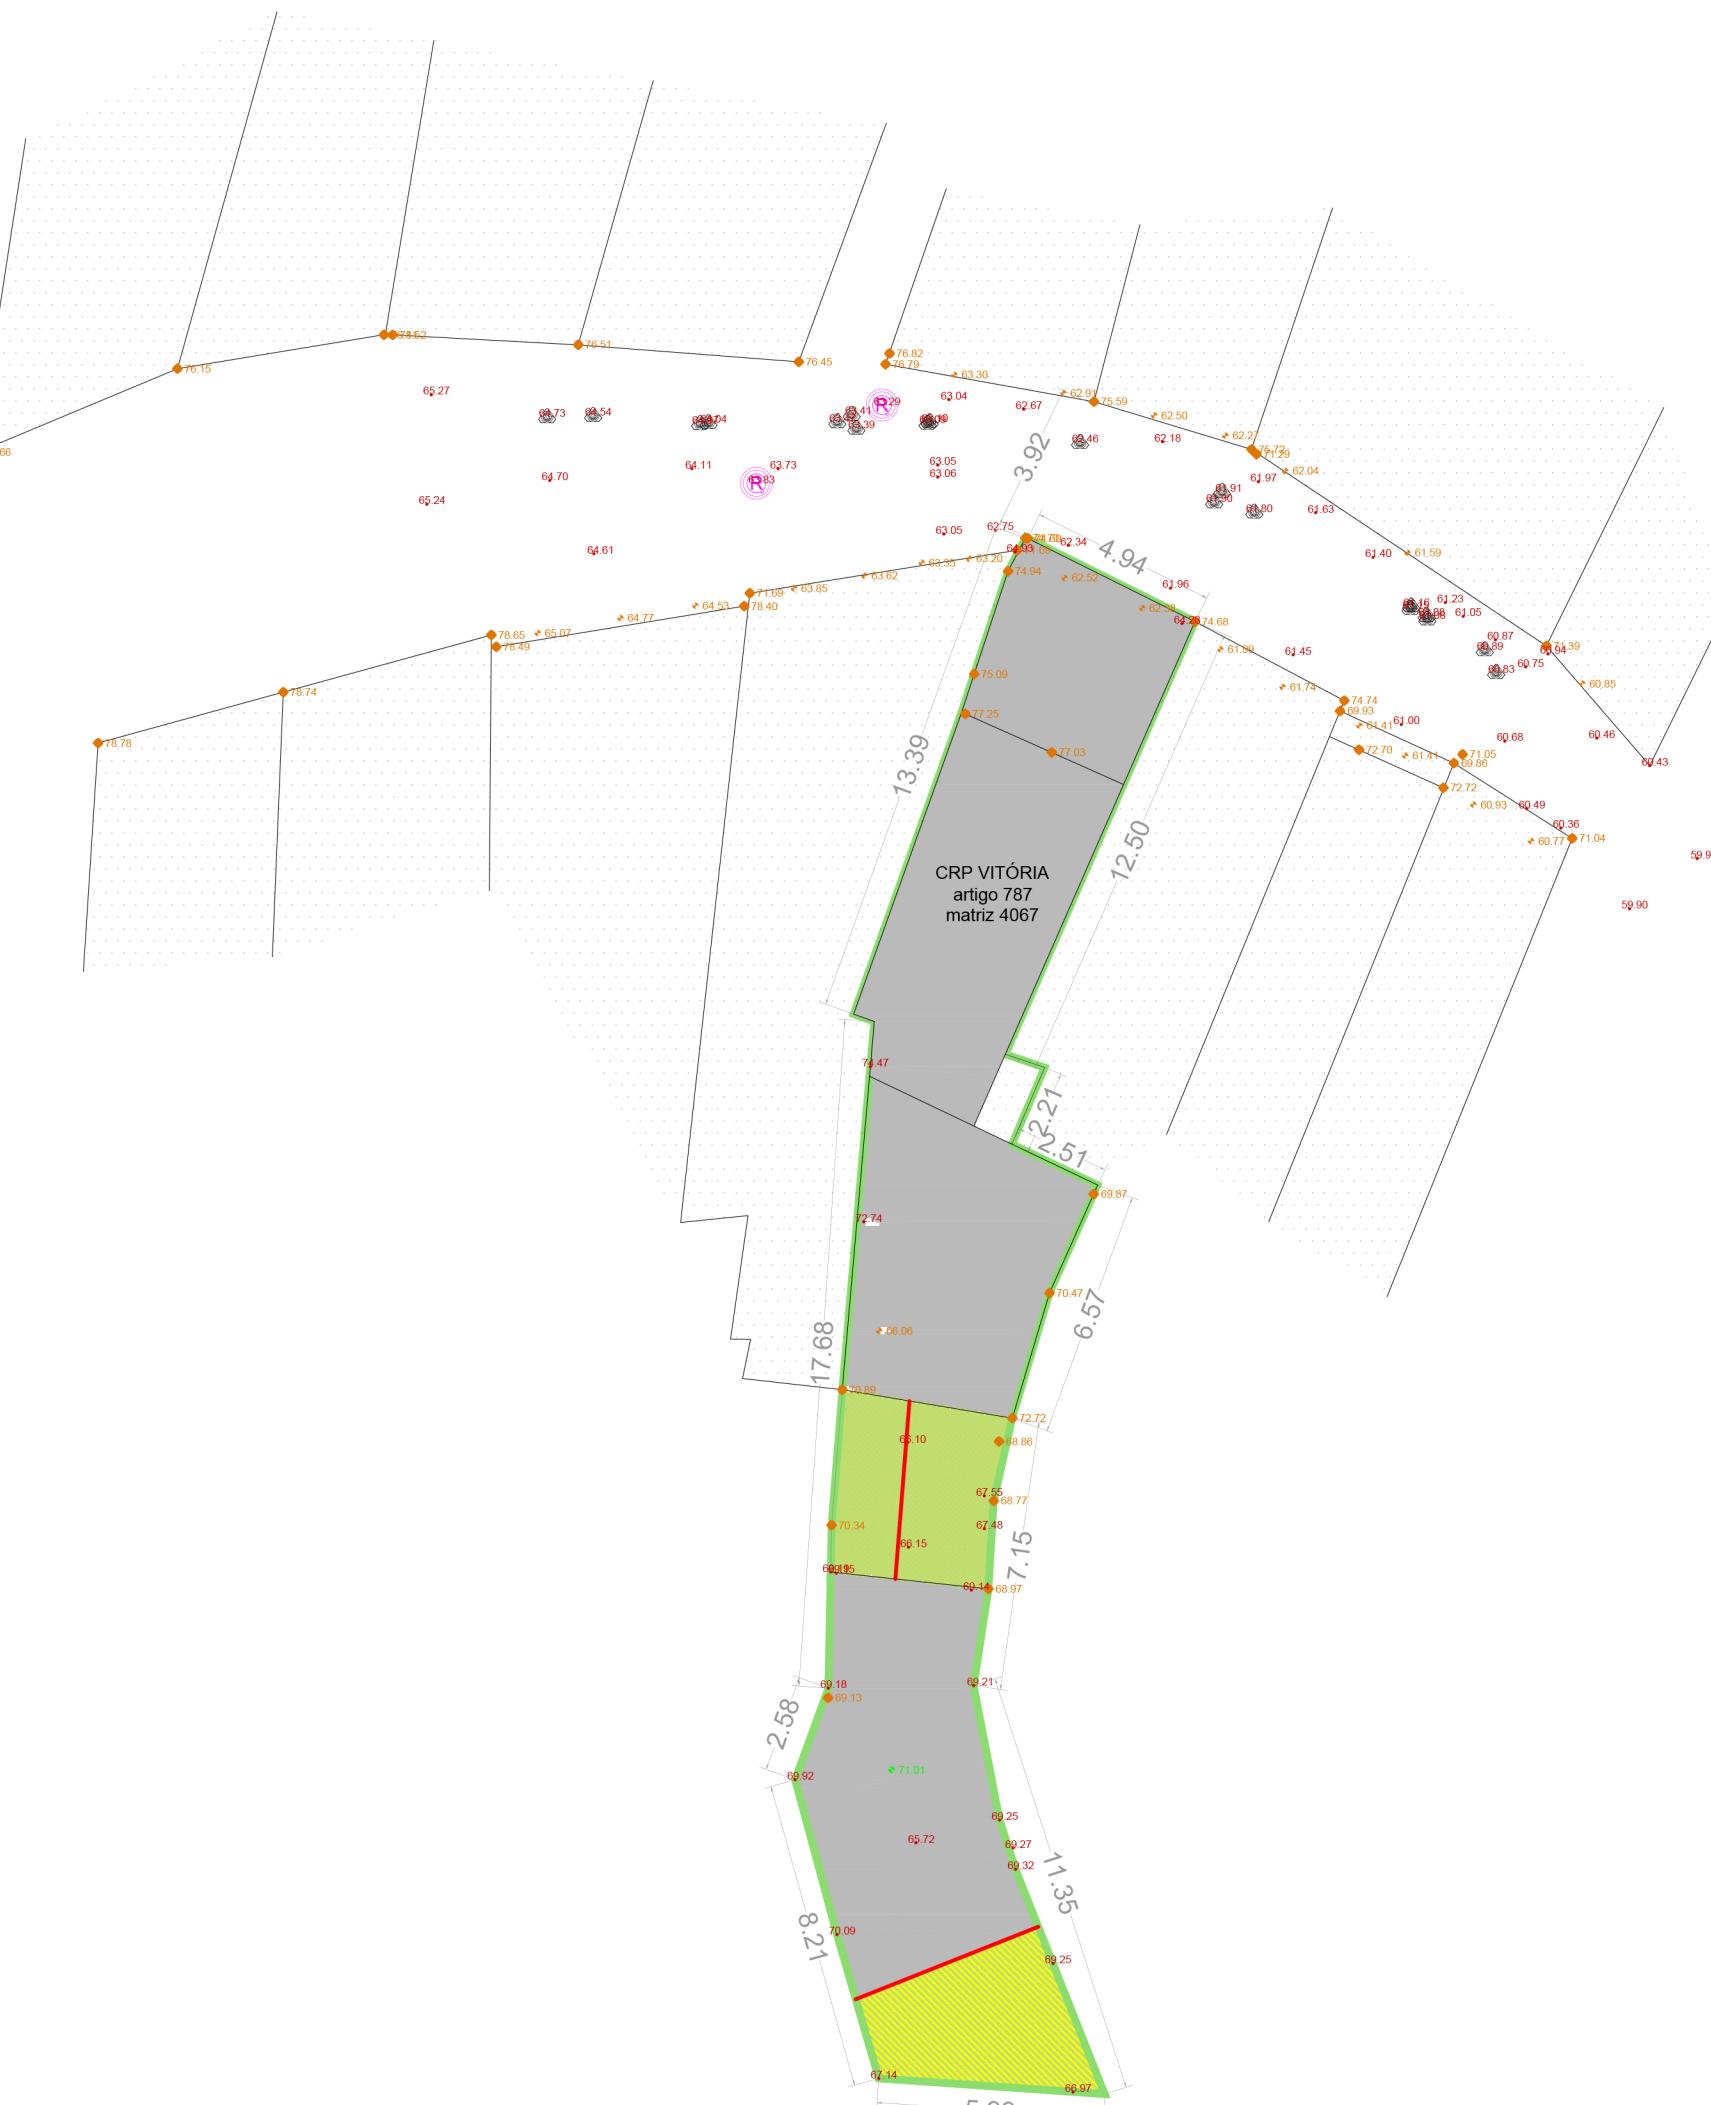


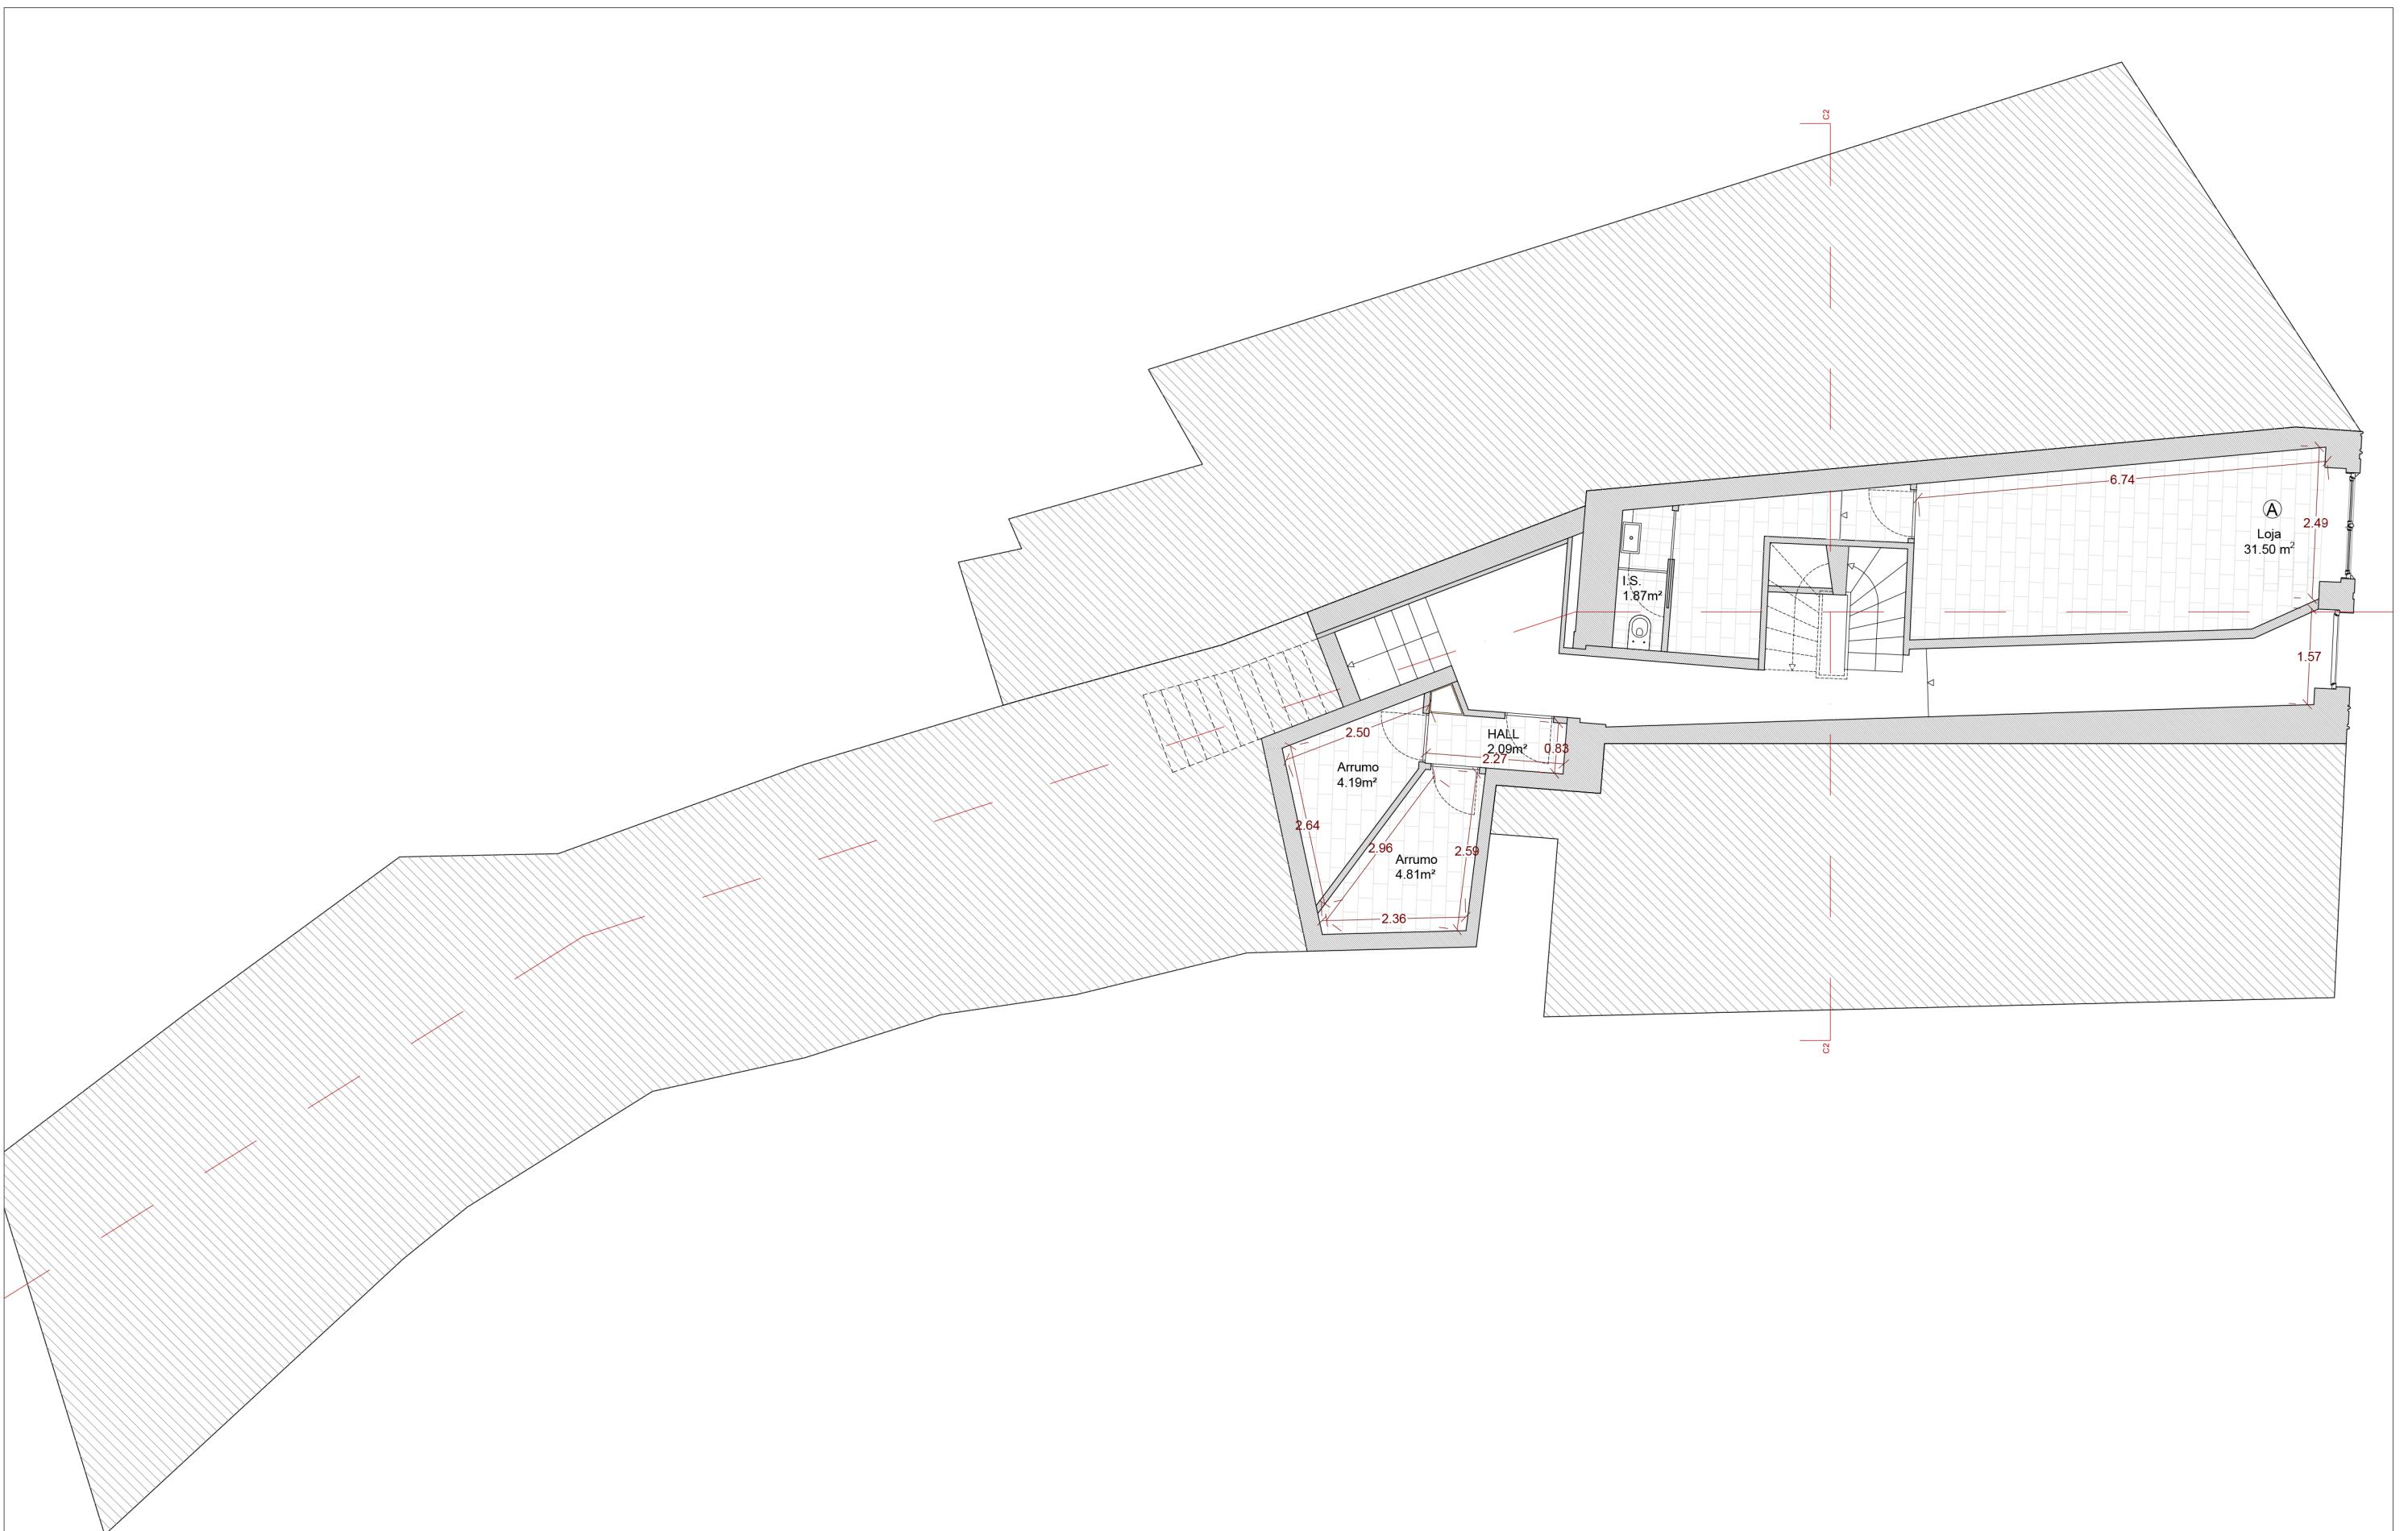

Planta Piso 0

10 November 2020

02

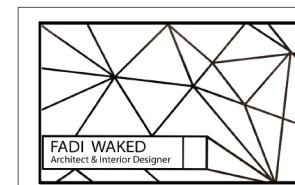


rua dos Caldeireiros, Porto



1|100
Escala

0 1.0 2.0 3.0m

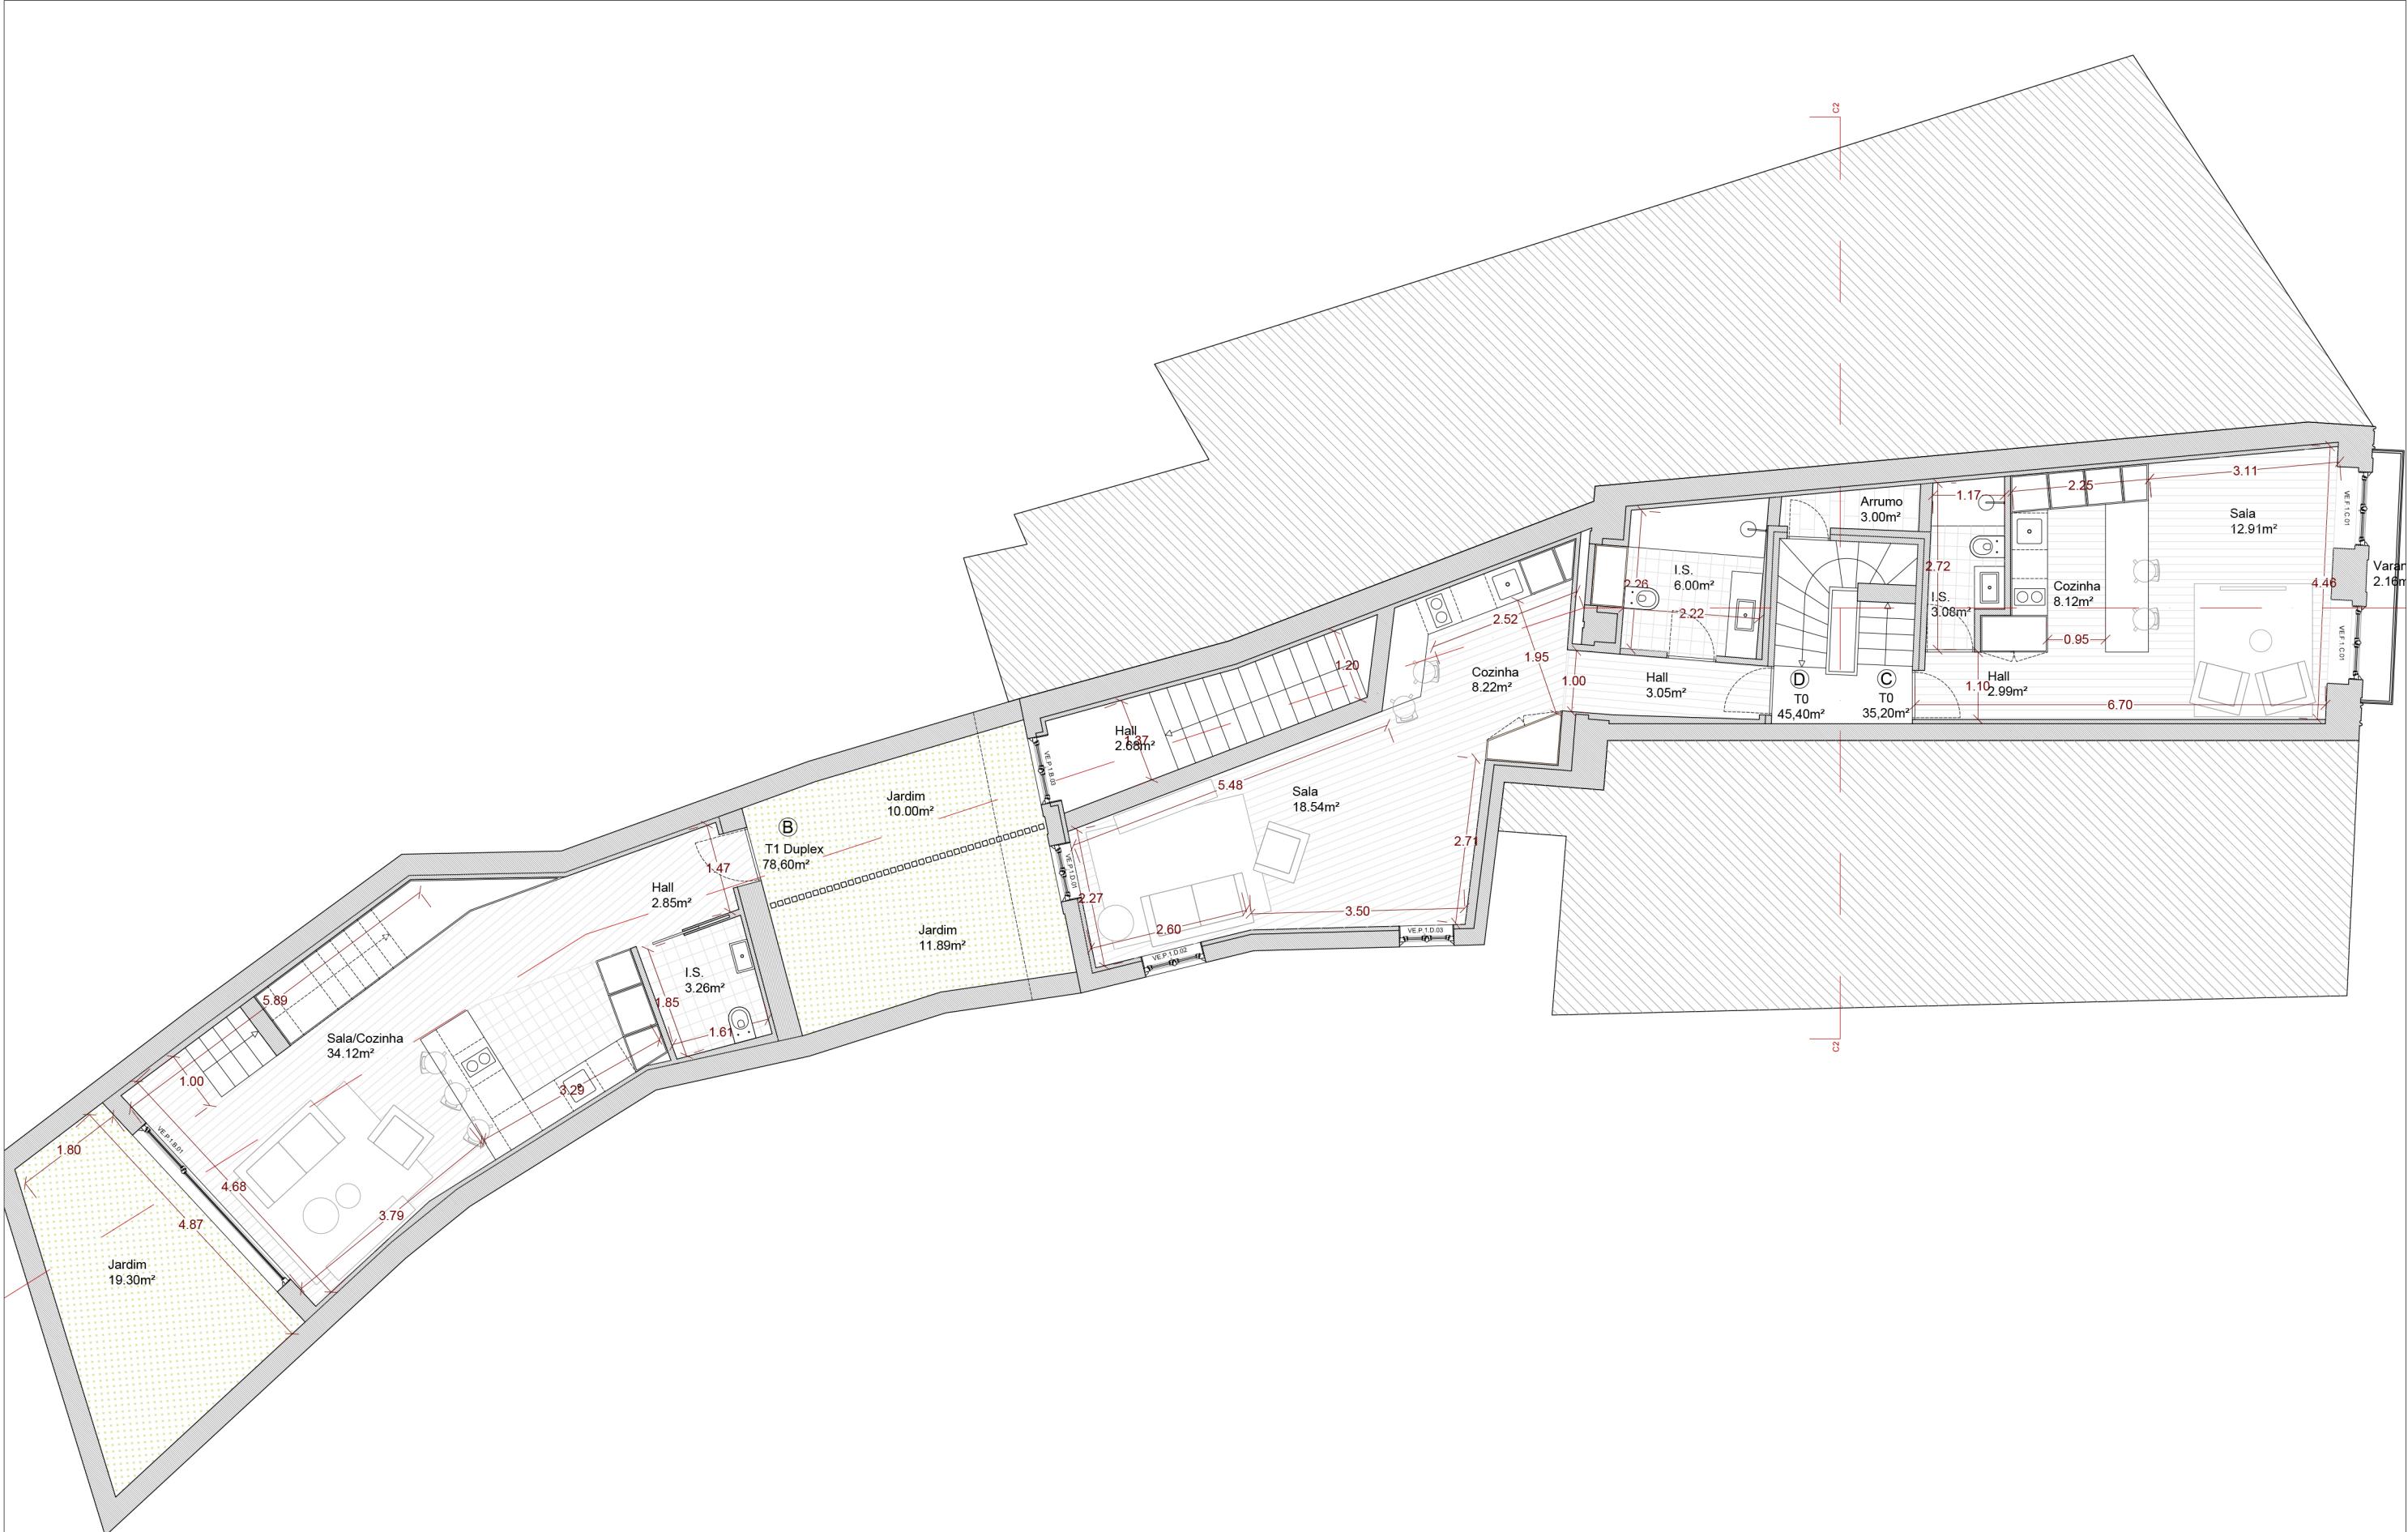


Planta Piso 1

rua dos Caldeireiros, Porto



1|100
Escala

0 1.0 2.0 3.0m

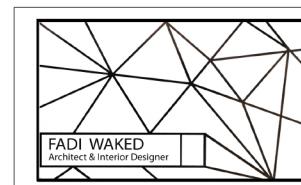

rua dos Caldeireiros, Porto





1|100
Escala

0 1.0 2.0 3.0m

Planta Piso 2
10 November 2020

04

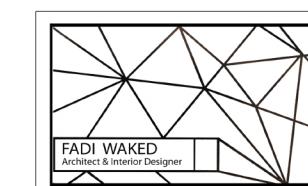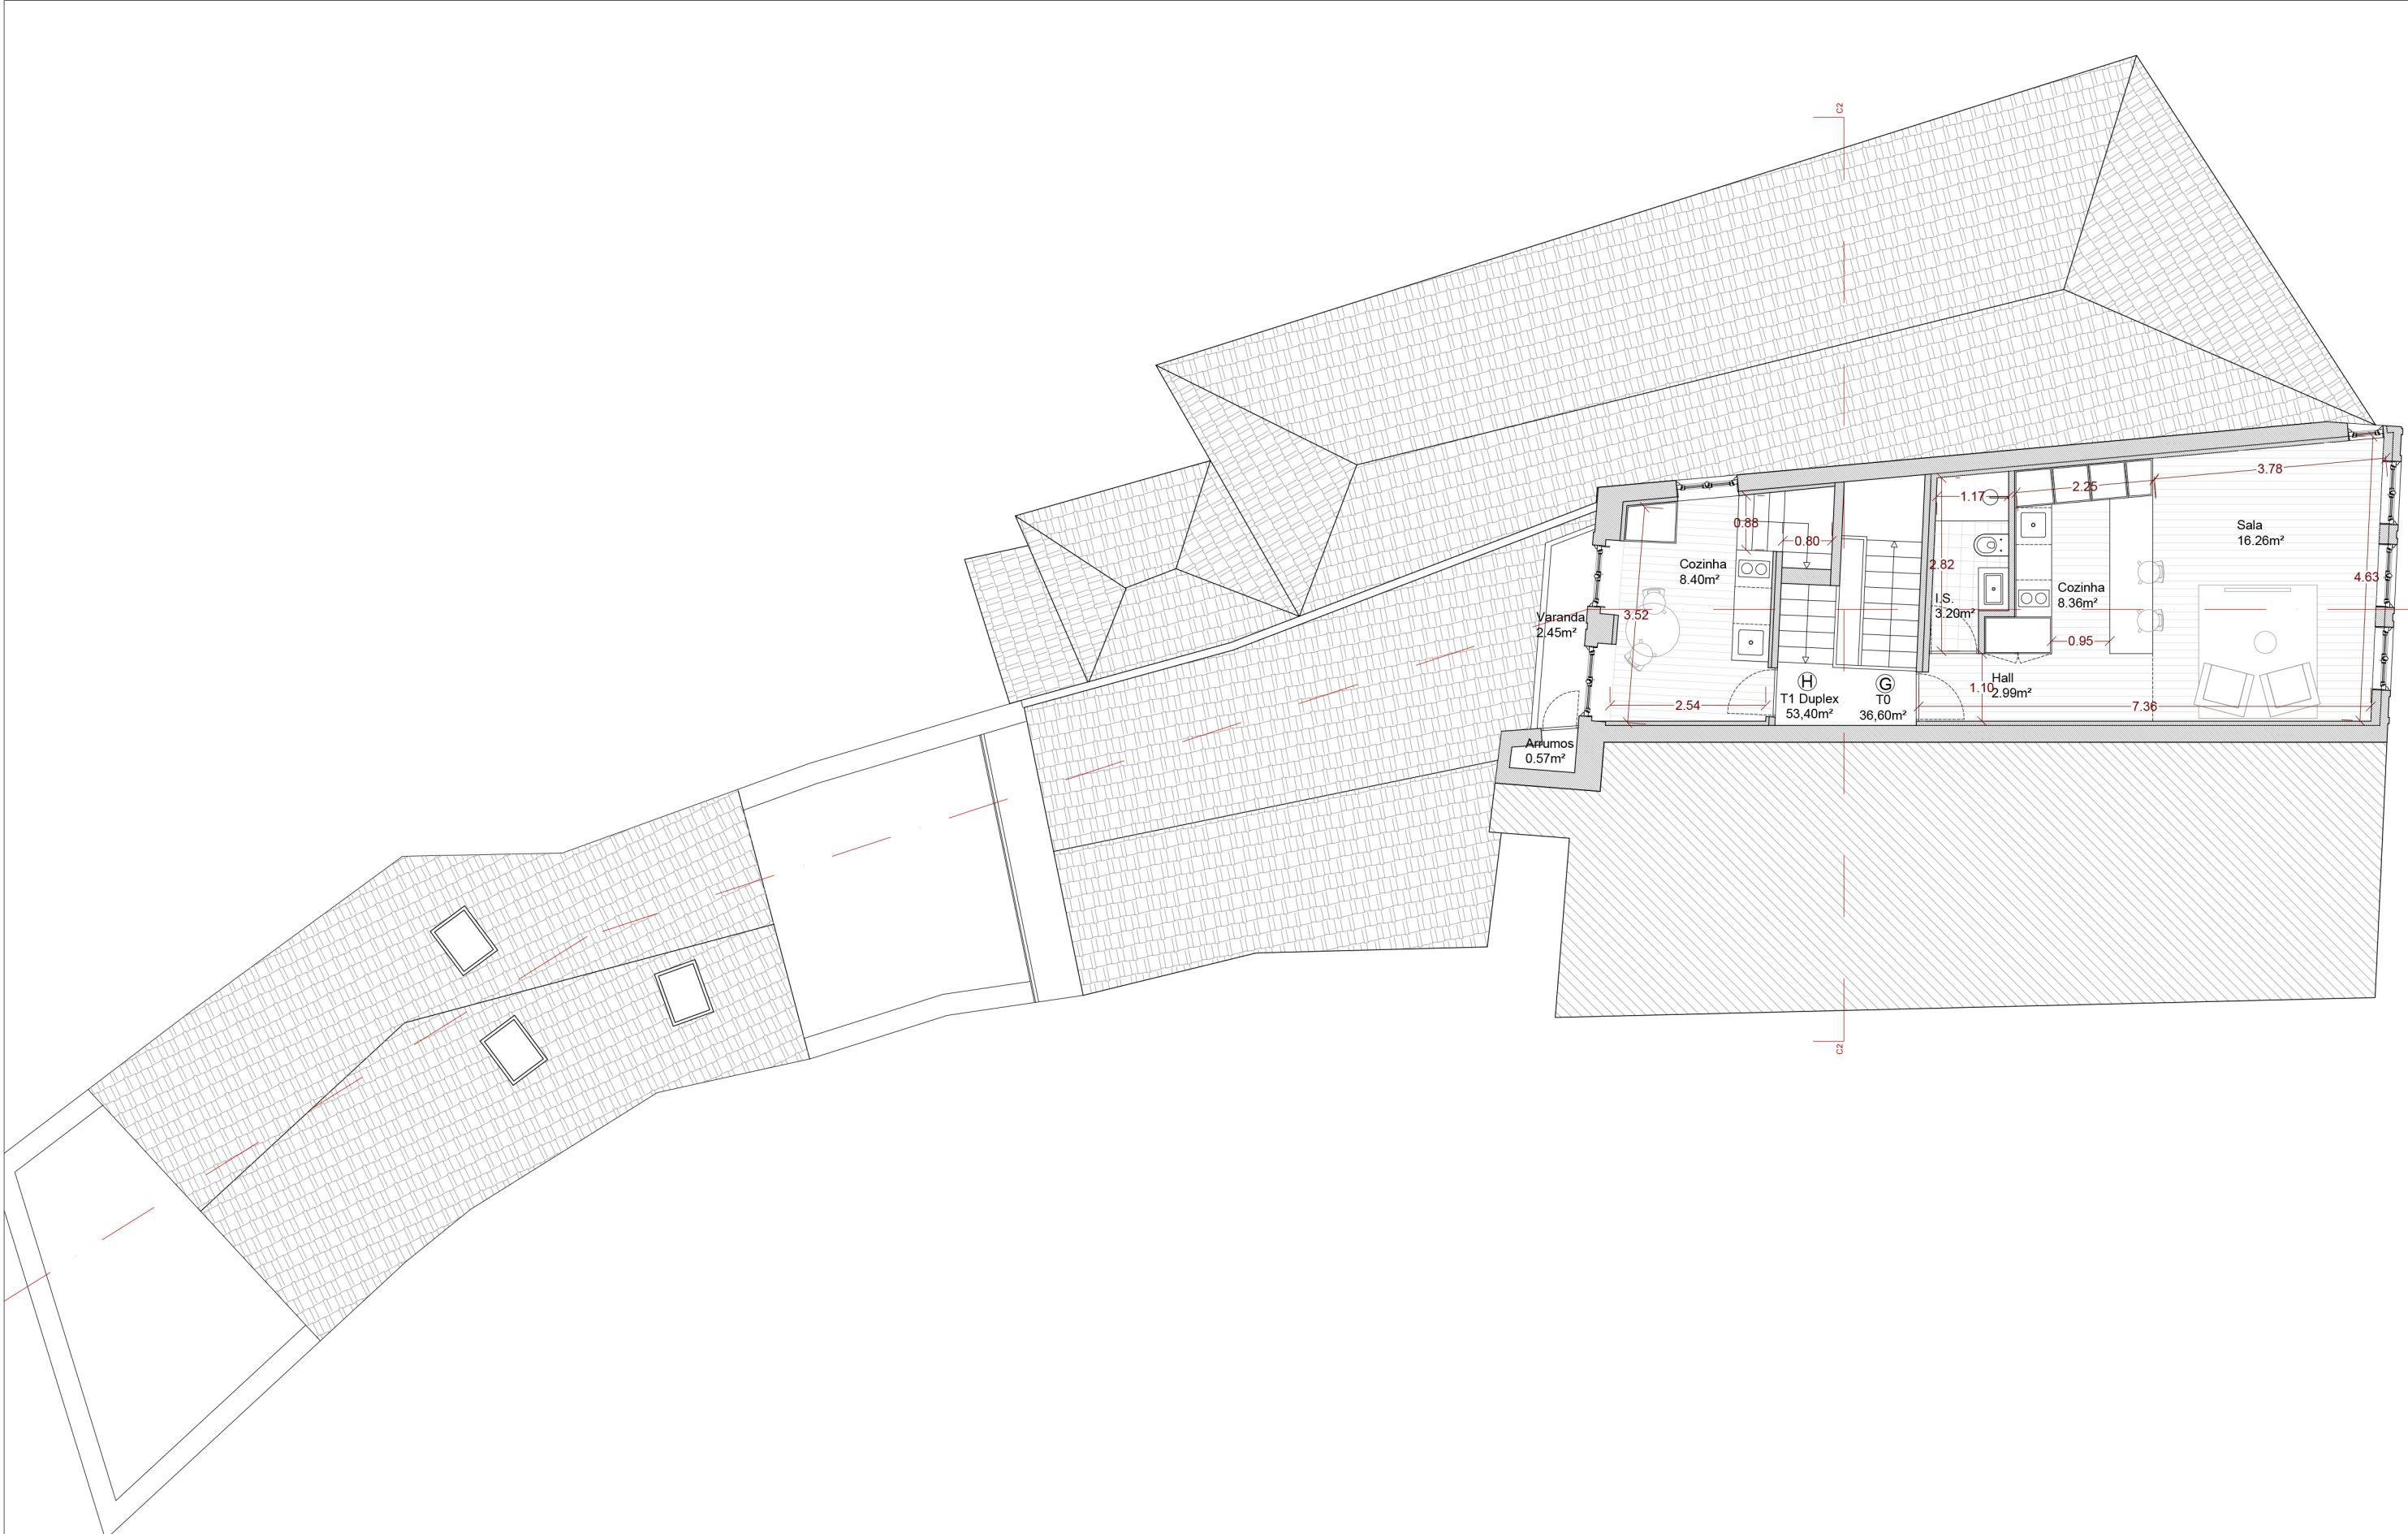



rua dos Caldeireiros, Porto



1|100

0 1.0 2.0 3.0m

05

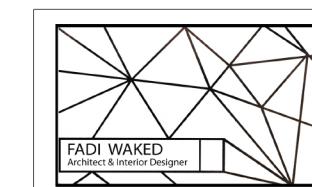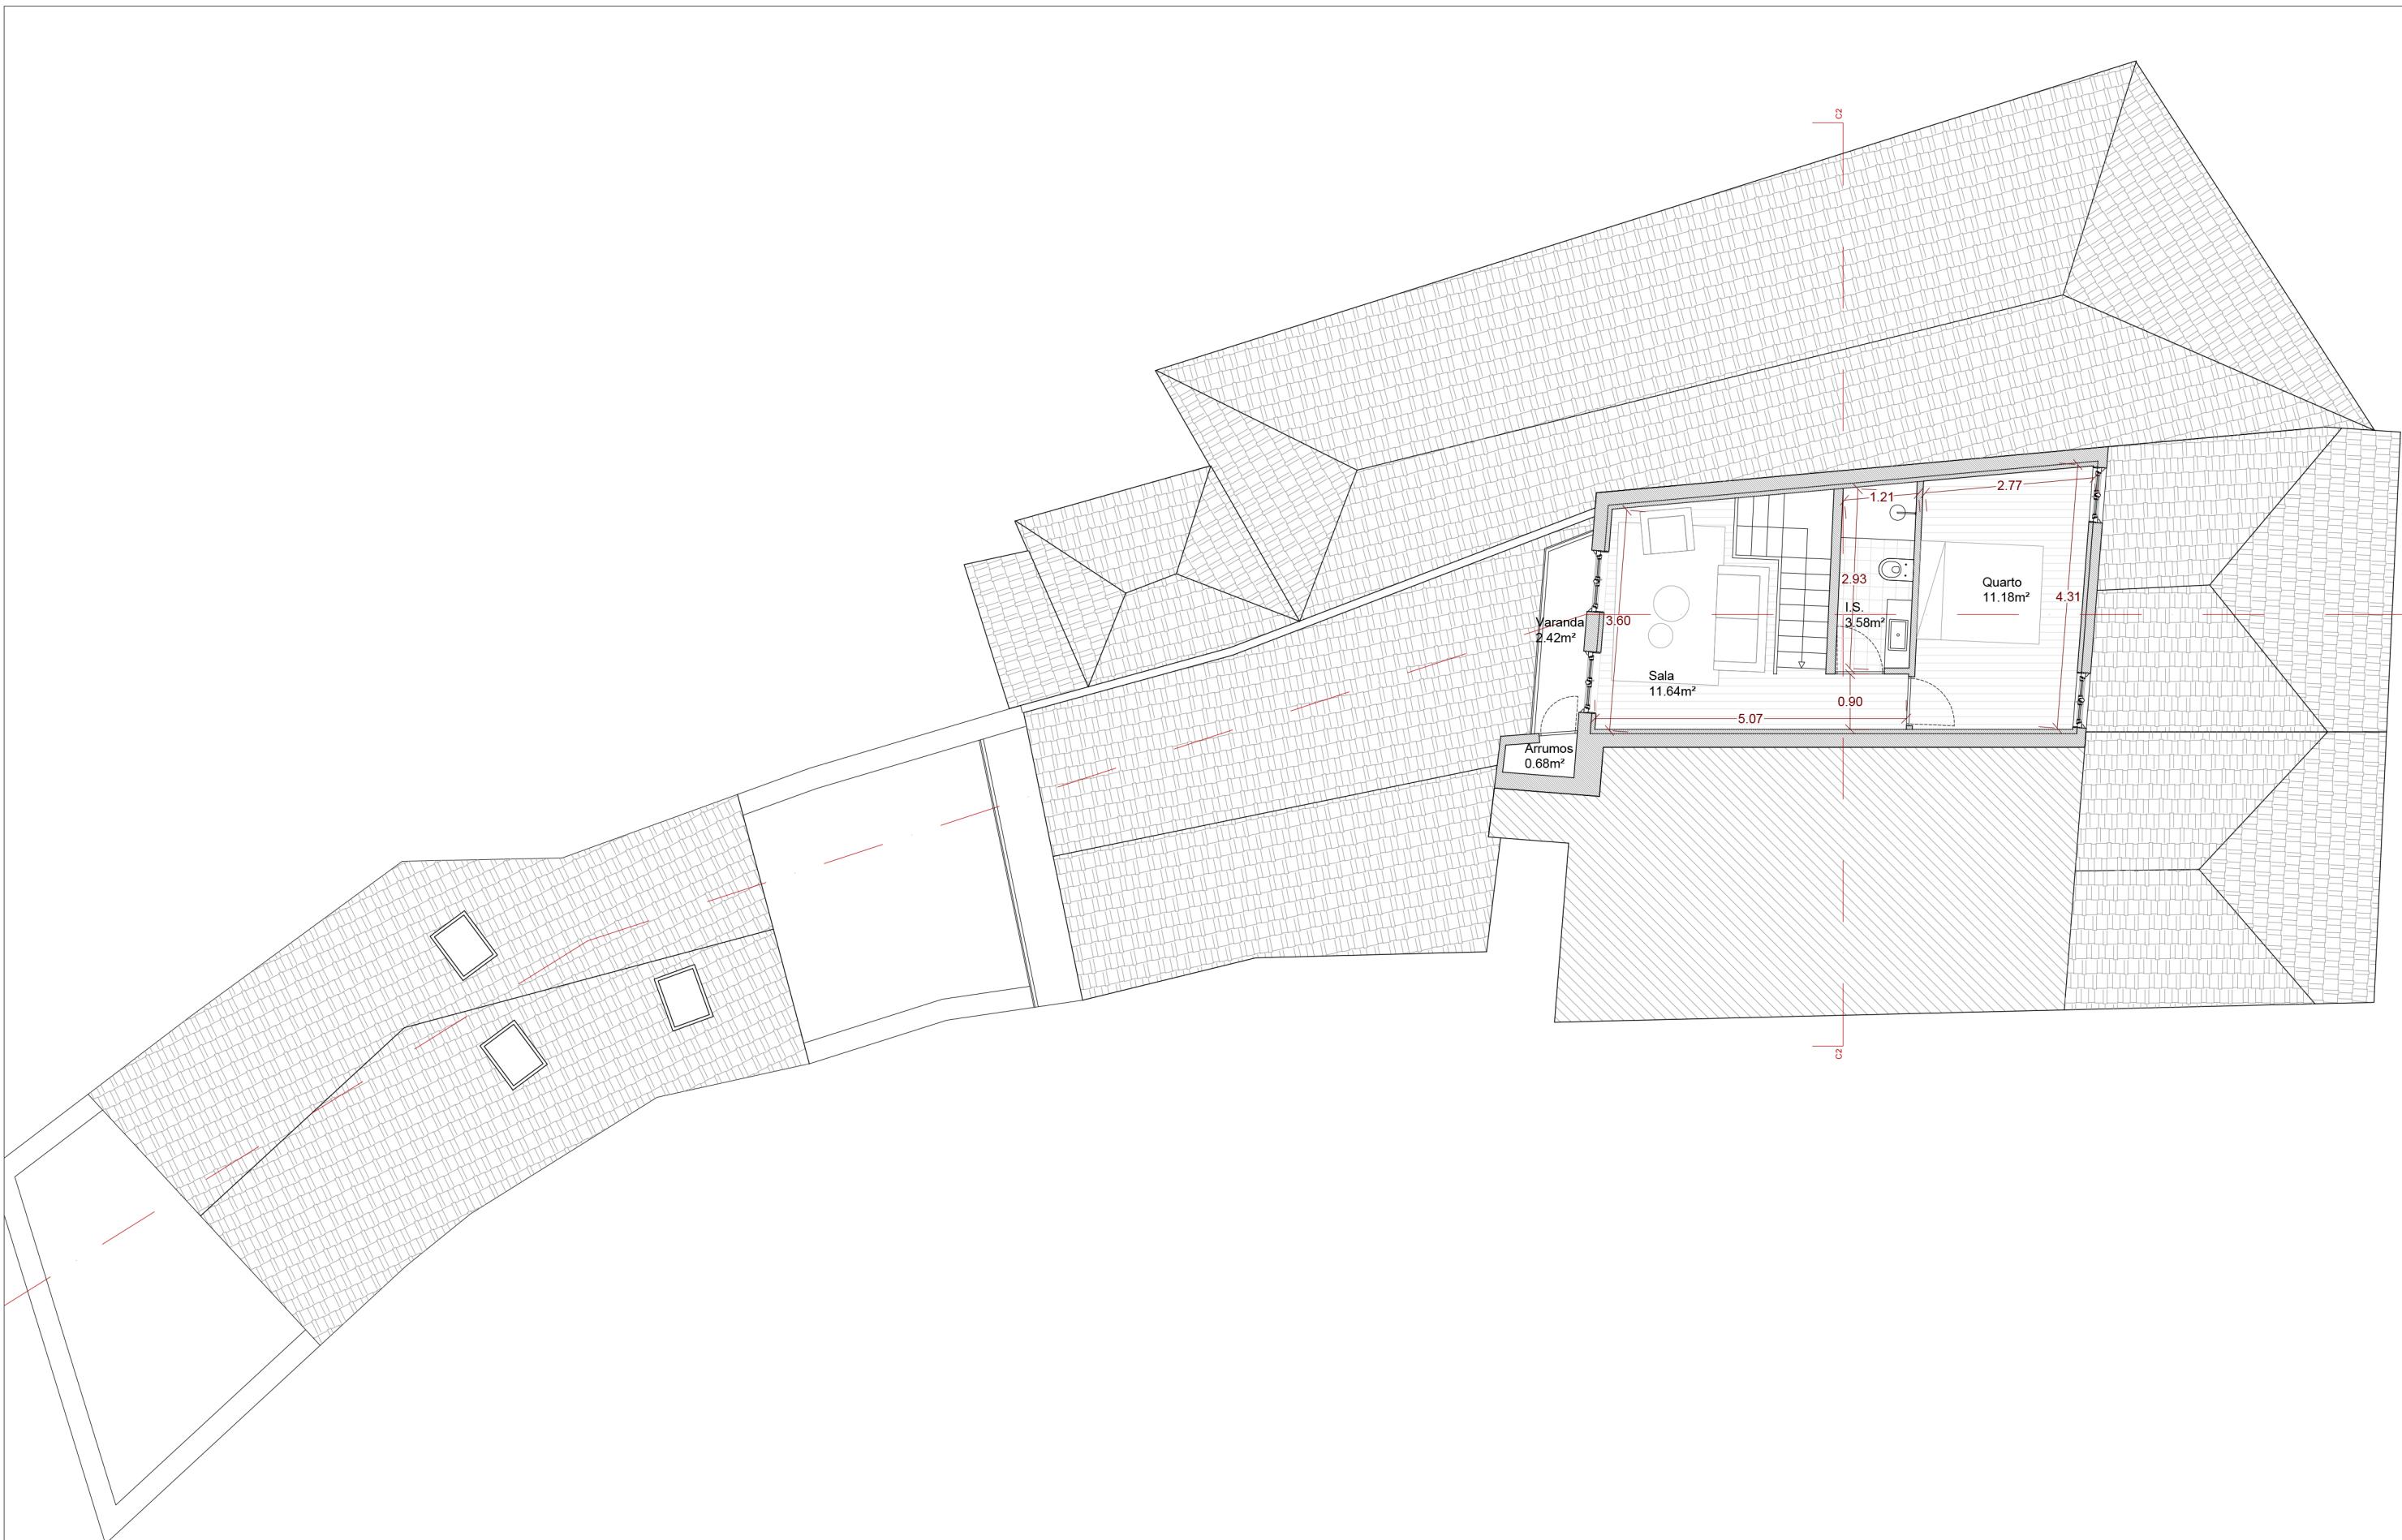

rua dos Caldeireiros, Porto





1|100

0 1.0 2.0 3.0m

Planta 4
20 November 2020

06

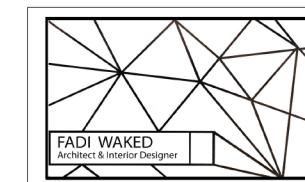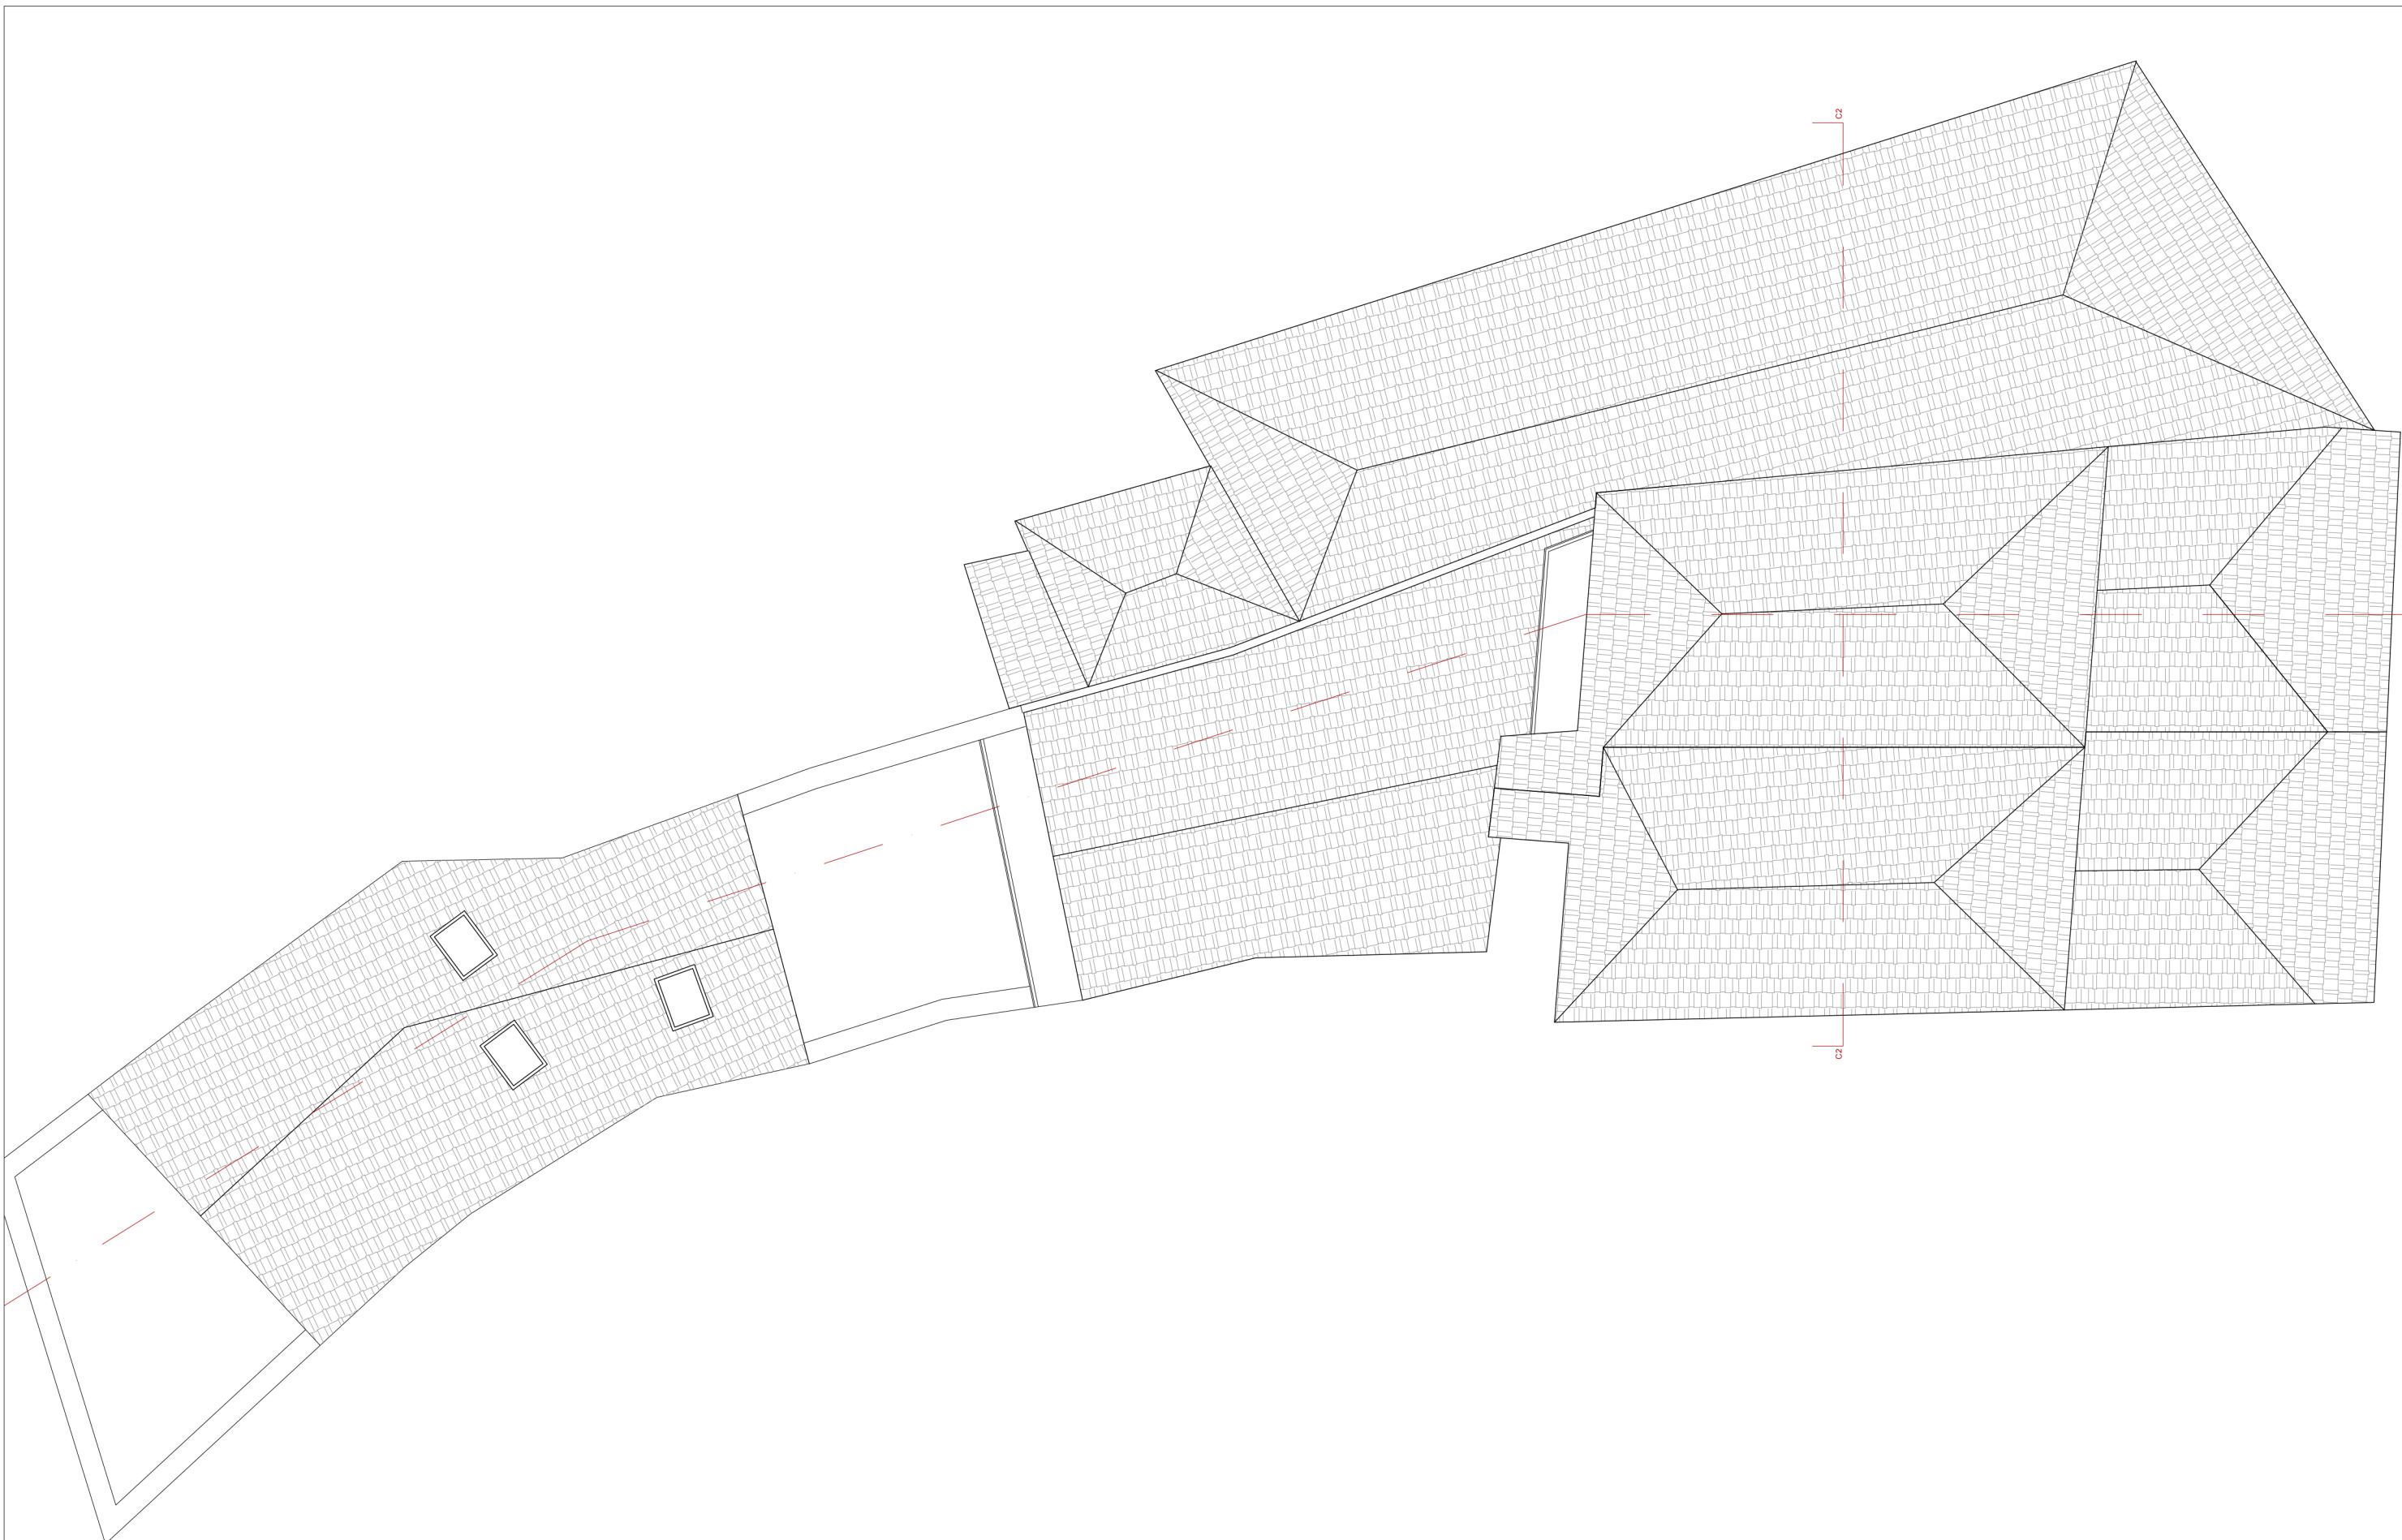

FADI WAKED
Architect & Interior Designer

rua dos Caldeireiros, Porto



1|100

0 1.0 2.0 3.0m

Planta Cobertura
20 November 2020